




GAMBAR ARSITEKTUR

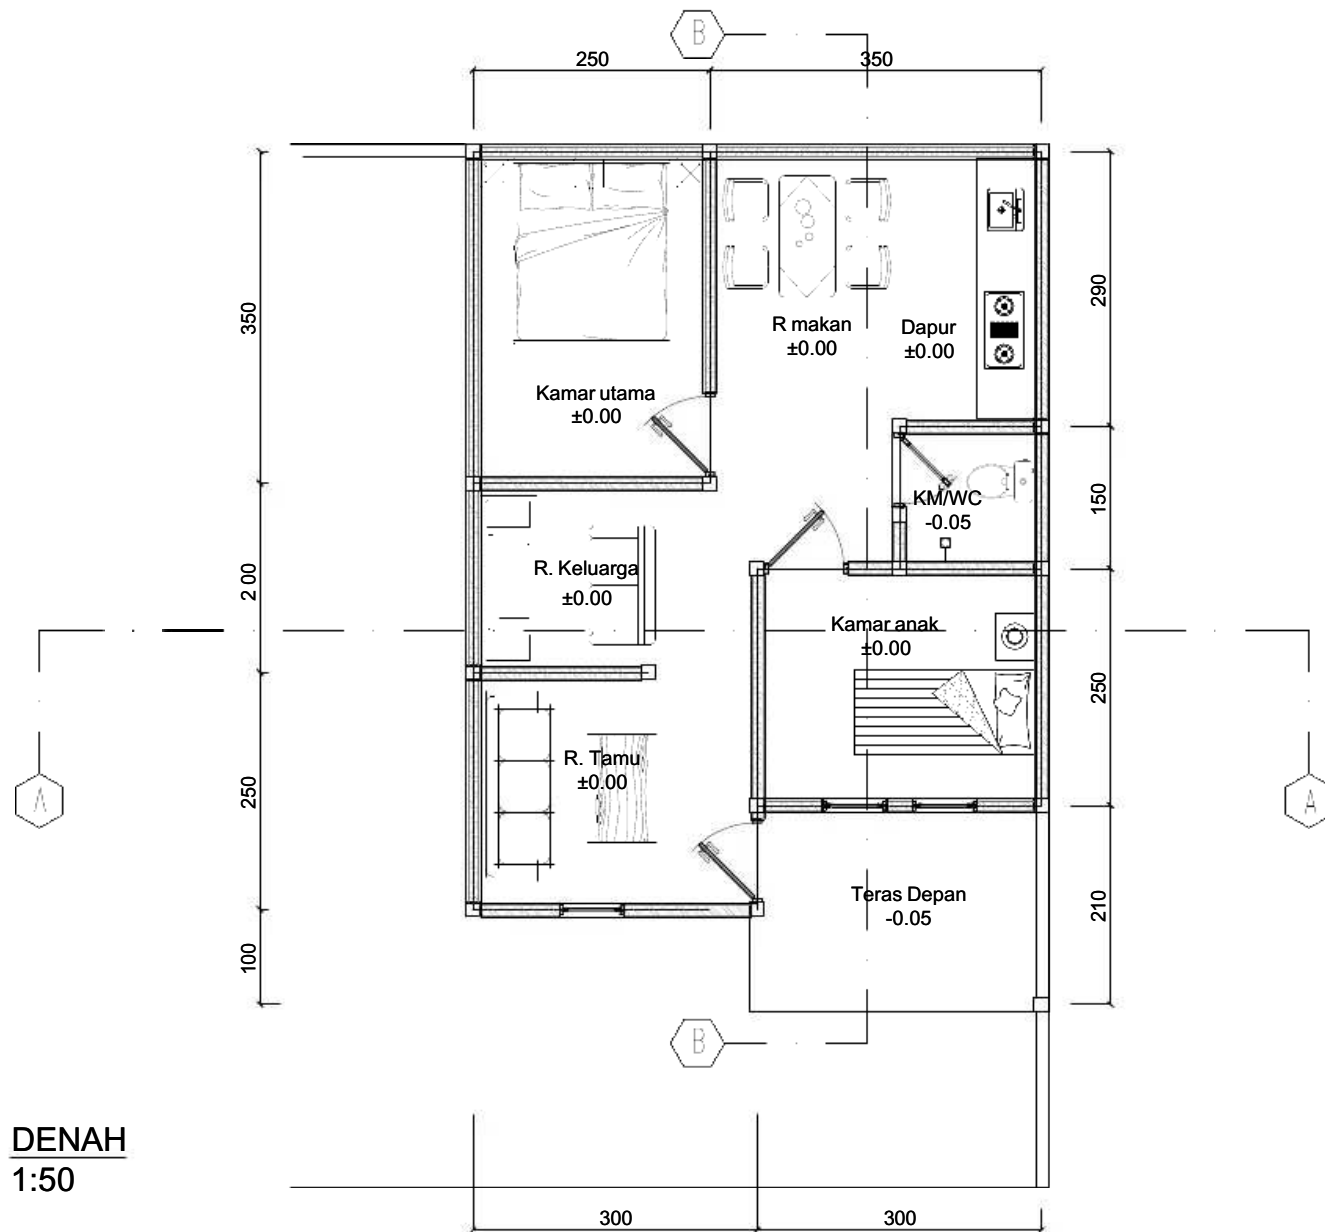


DENAH
1:50

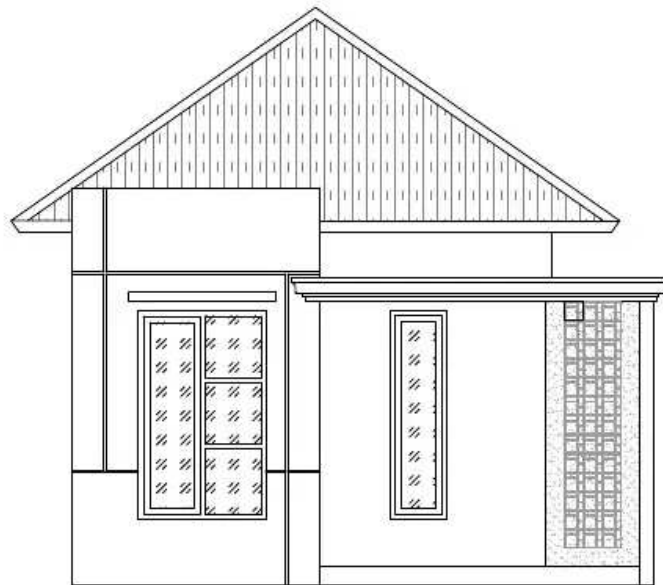


TAMPAK DEPAN
1:50

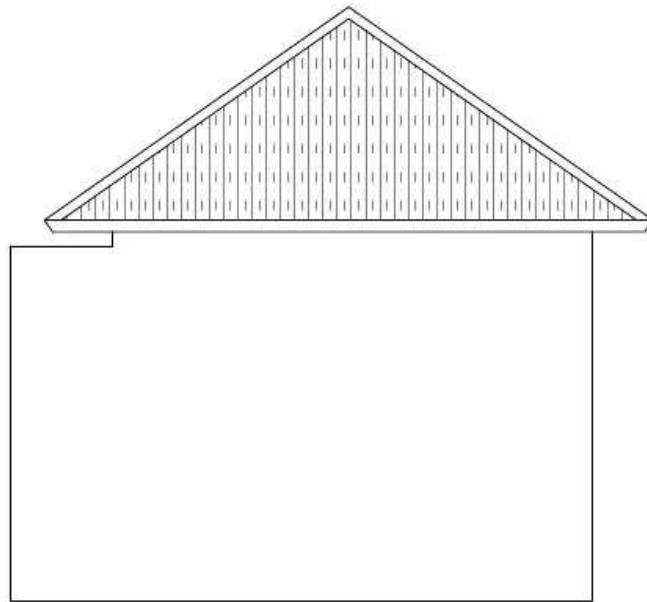


TAMPAK BELAKANG
1:50

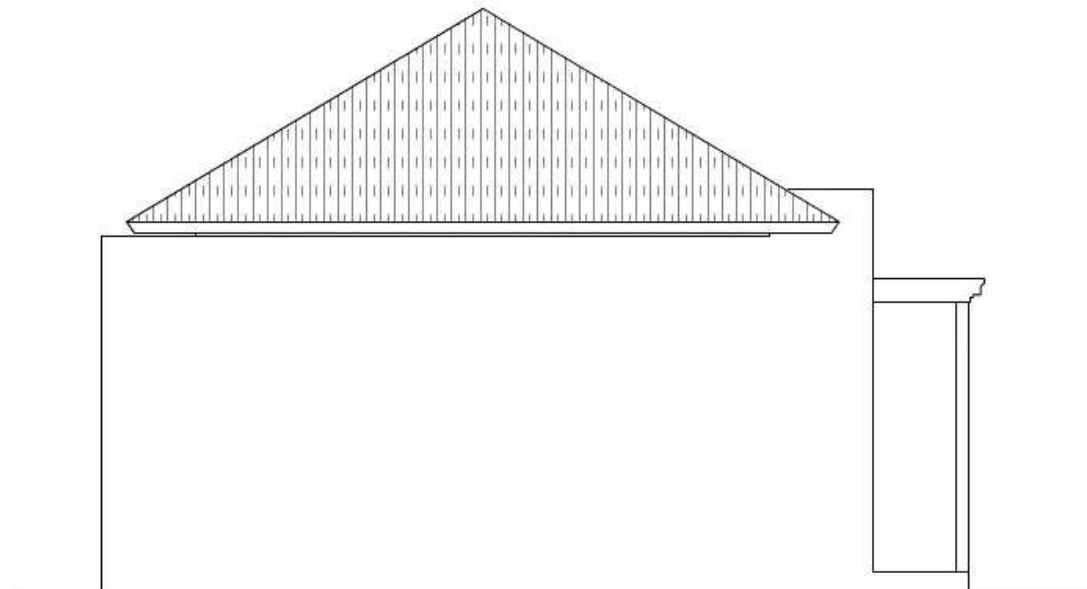


TAMPAK SAMPING KANAN
1:50

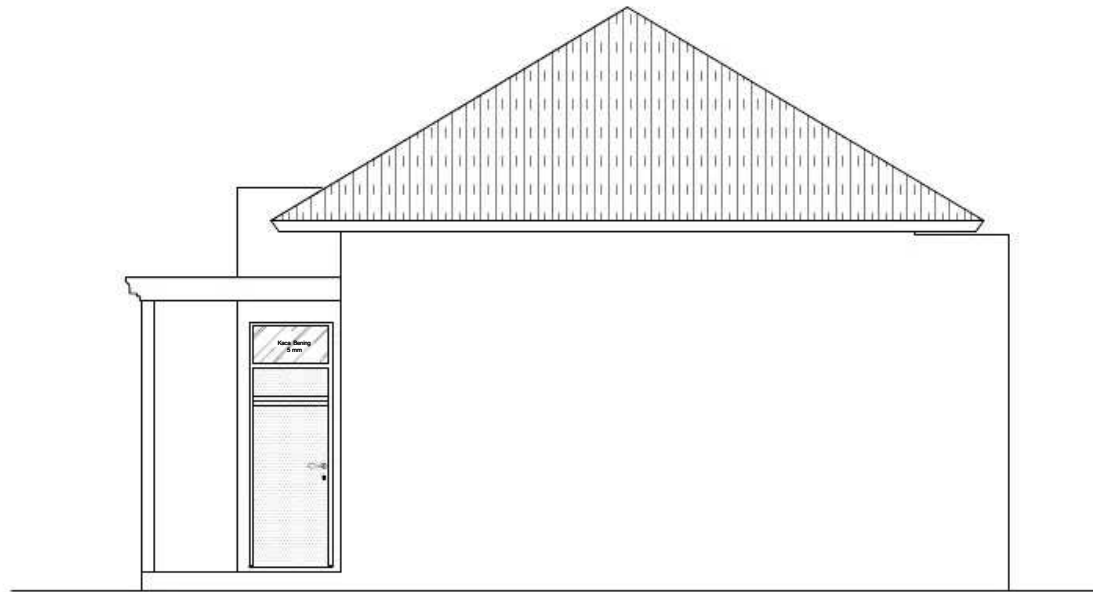

TAMPAK SAMPING KIRI
1:50

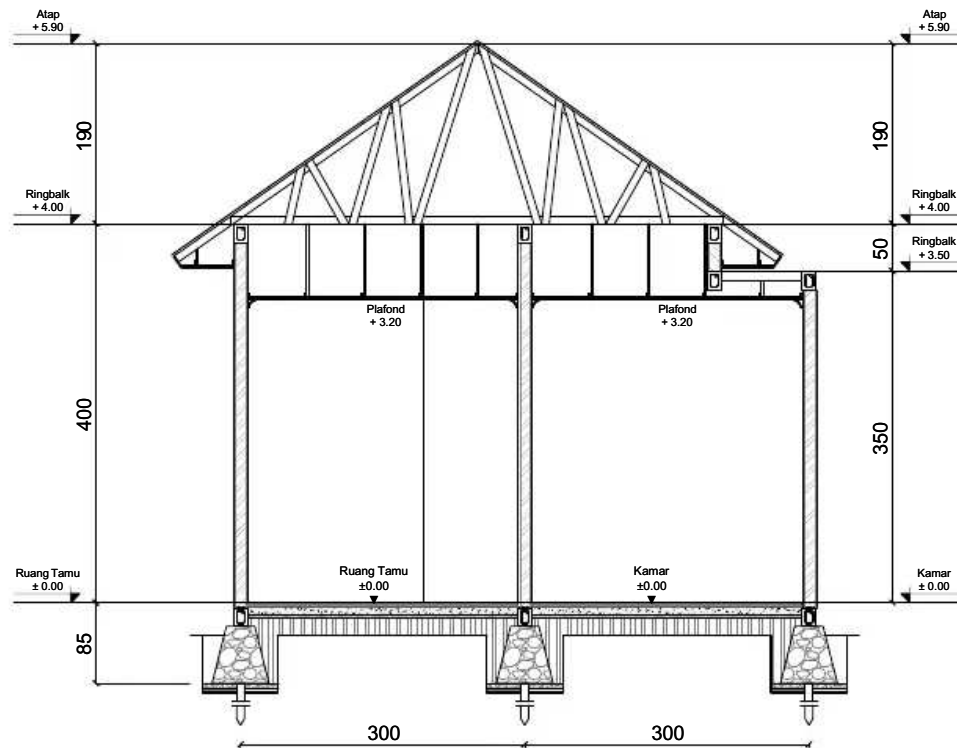








POTONGAN A-A
1:50

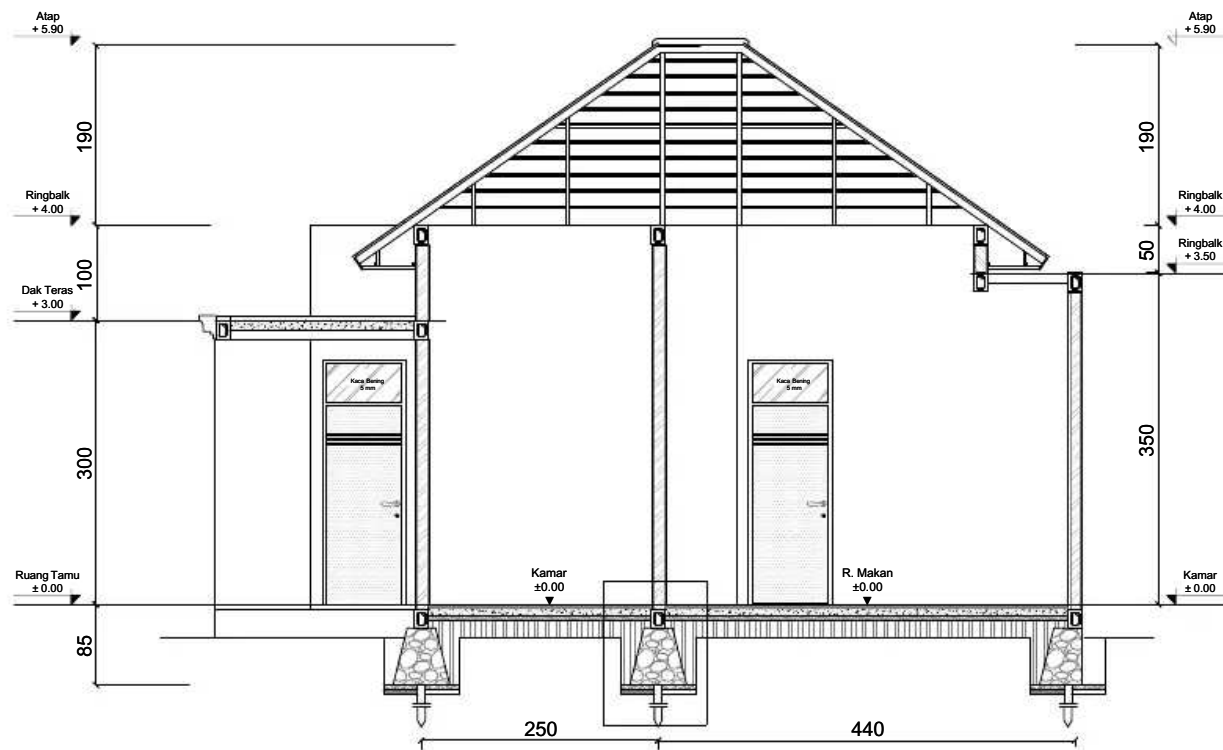


POTONGAN B-B
1:50

DENAH KUSEN
1:50

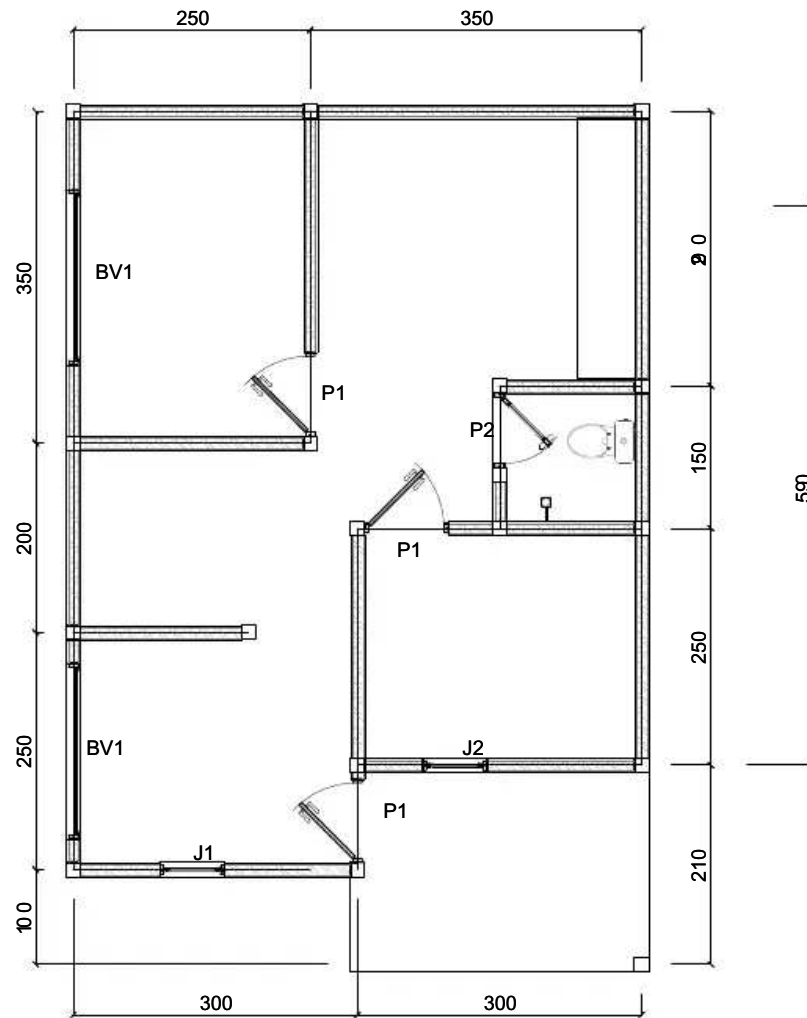


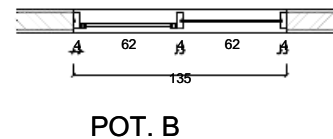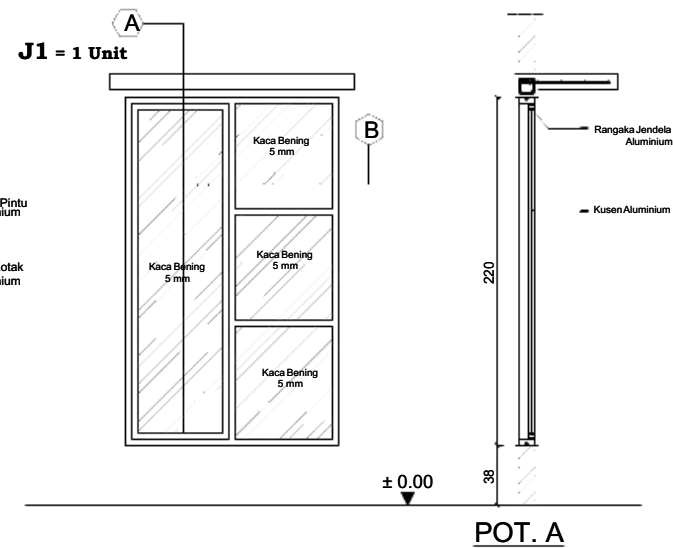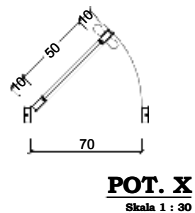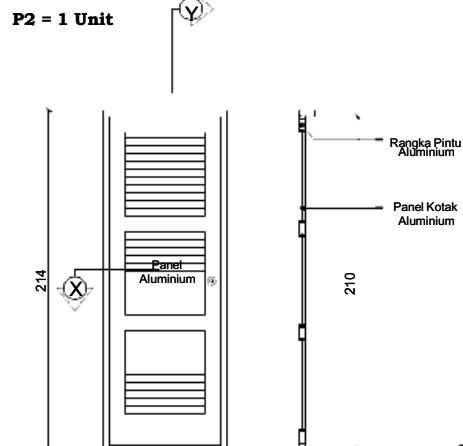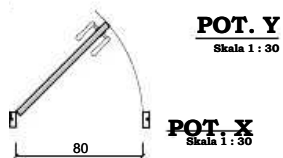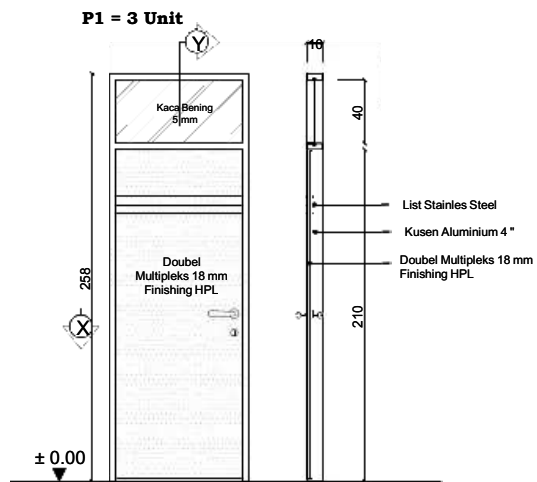


J2 = 1 Unit

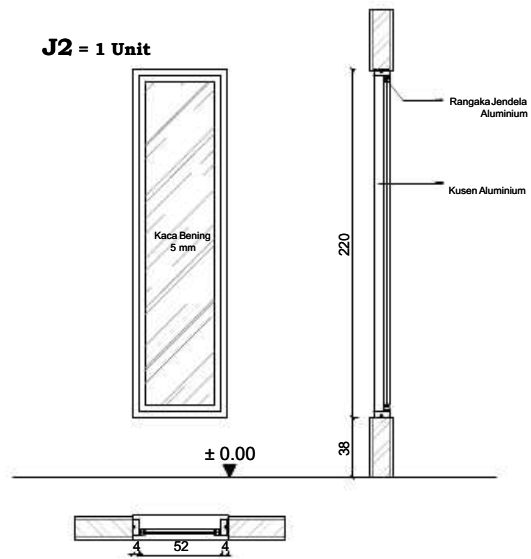


J3 = 2 Unit

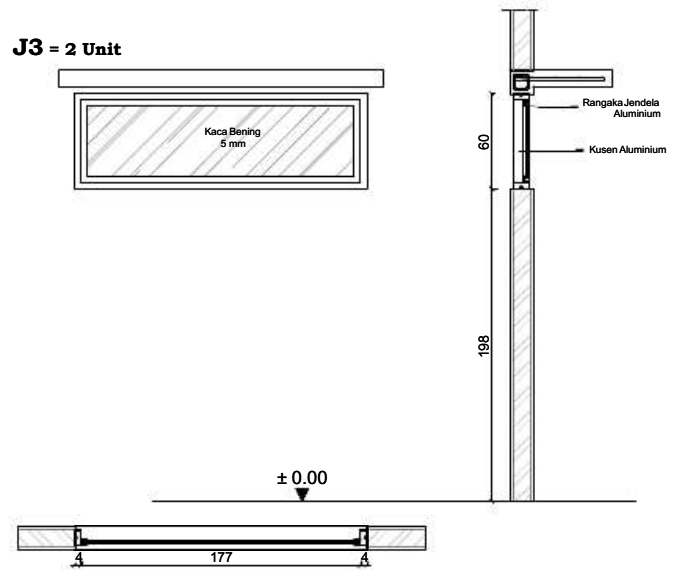


DENAH KERAMIK
1:50

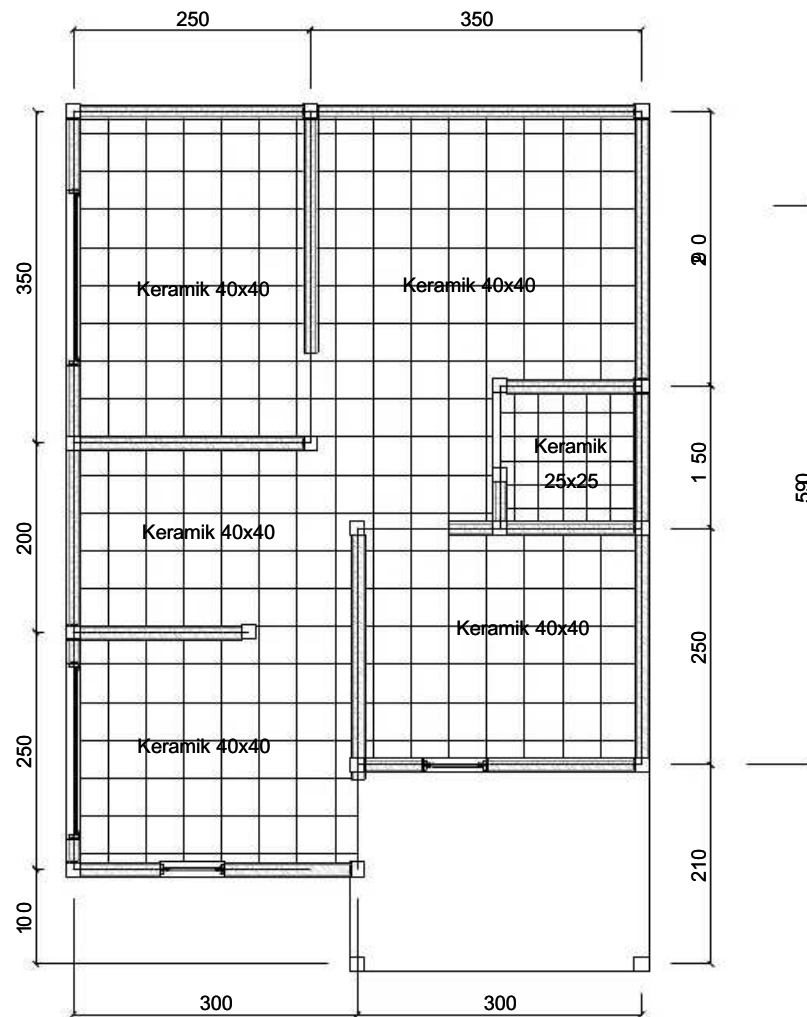


DENAH PLAFOND
1:50

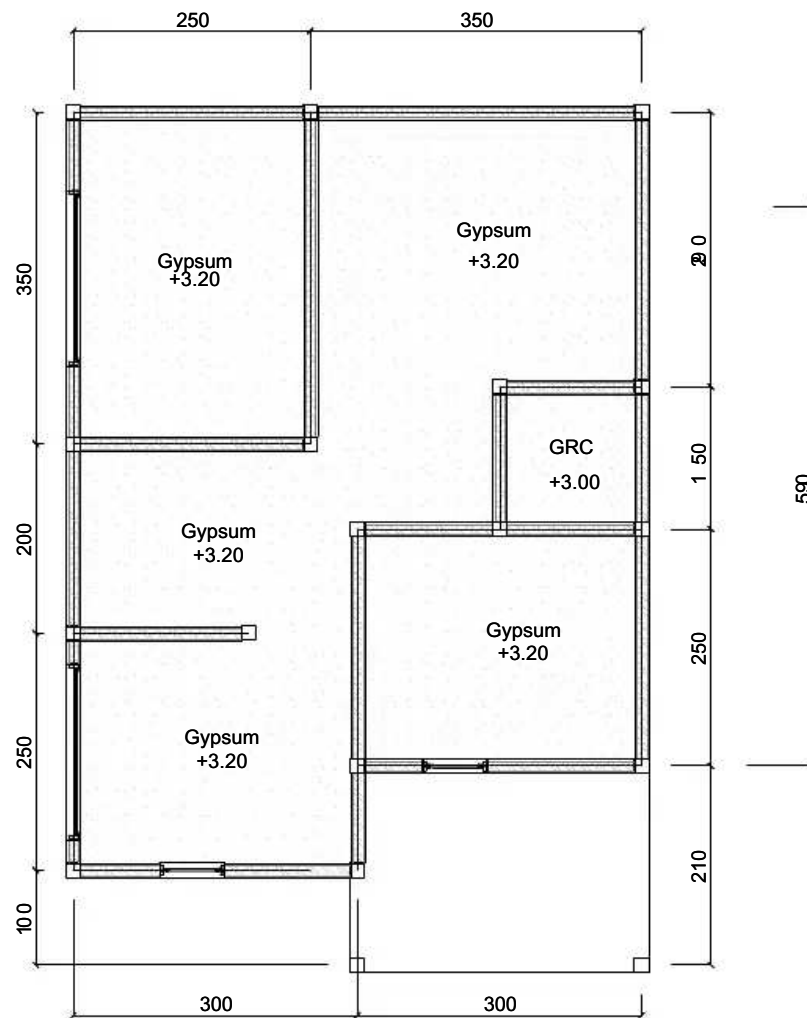

NOTASI	KETRANGAN
MS	Atap Metal Spandek
KK	Kuda - Kuda Baja Ringan
R	Reng Baja Ringan
L	Listplank Kalsium Silikat Board 8 X 150 mm
NS	Nok Spandek

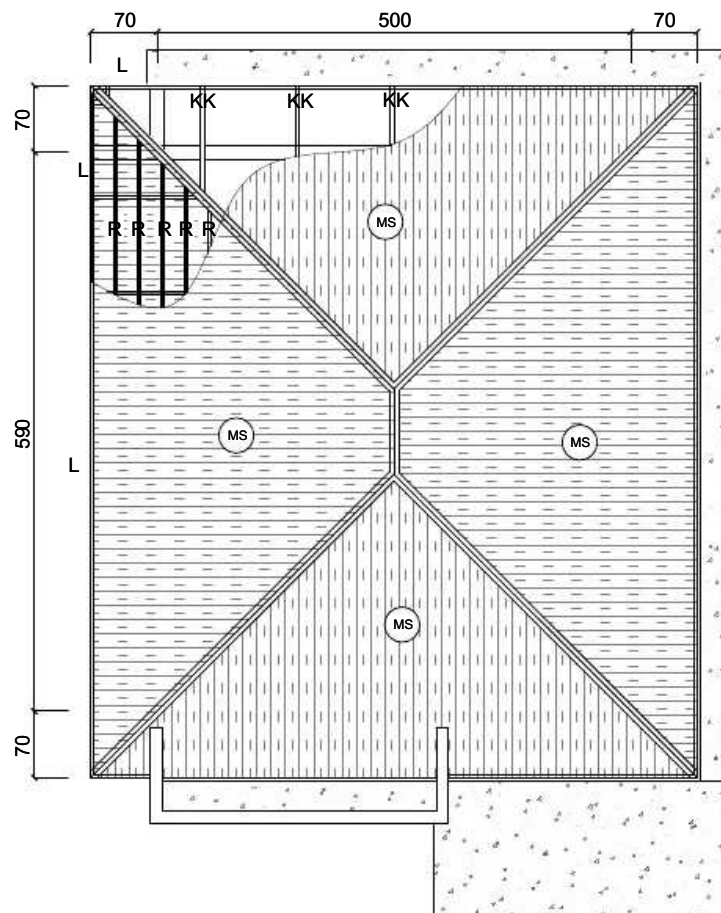


DENAH ATAP
1:50

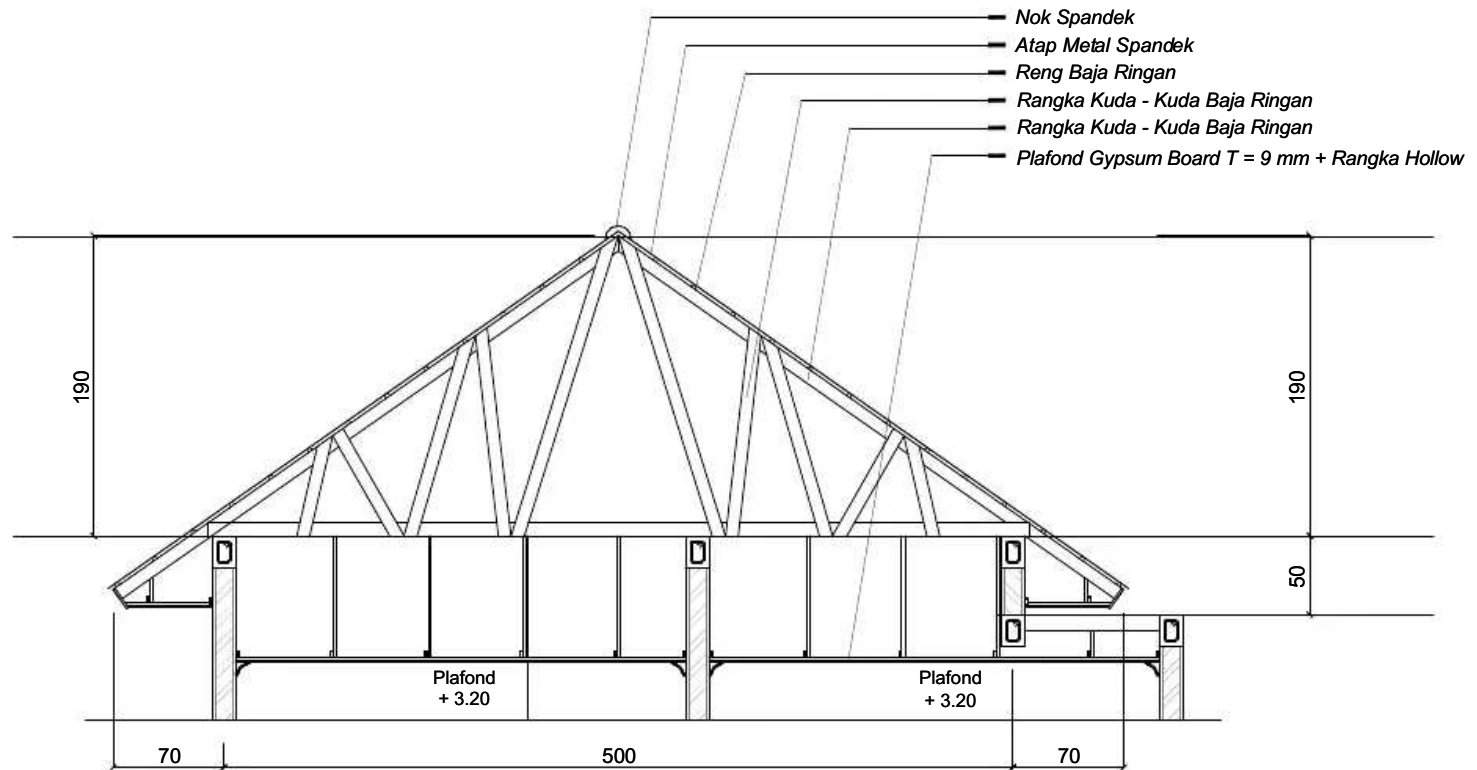


DETAIL ATAP


1:30

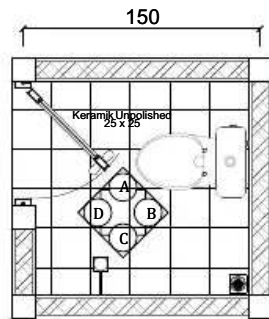


DENAH WC
1:30

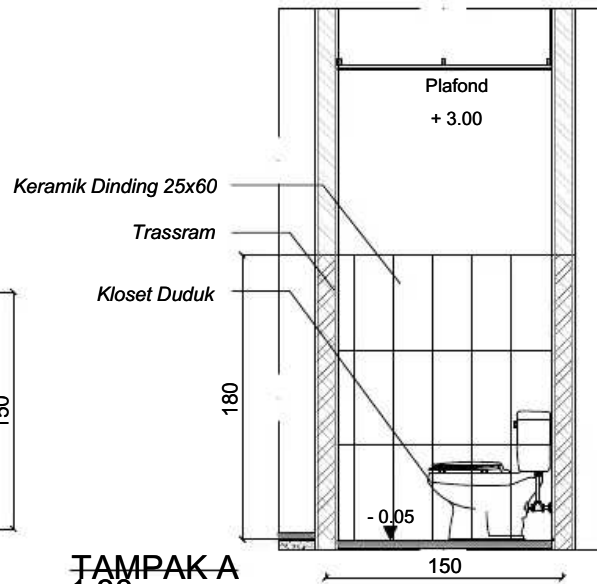


TAMPAK A
1:30

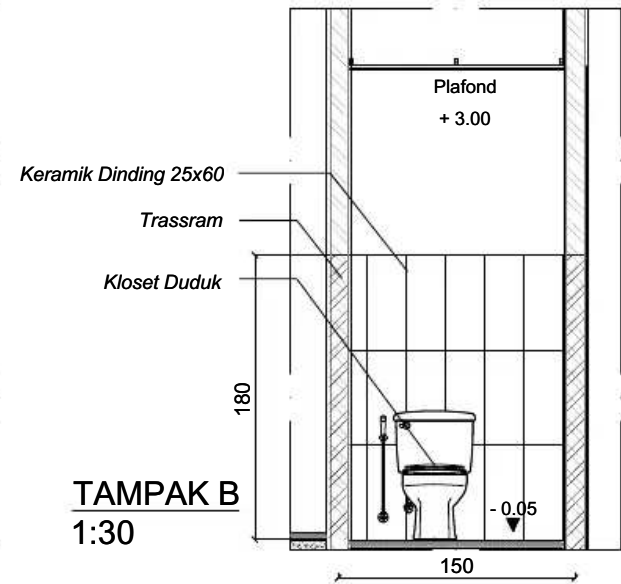

TAMPAK B
1:30

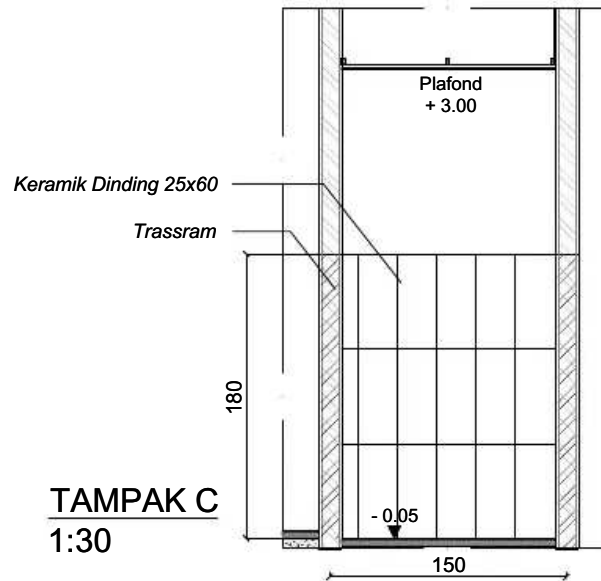


TAMPAK C
1:30

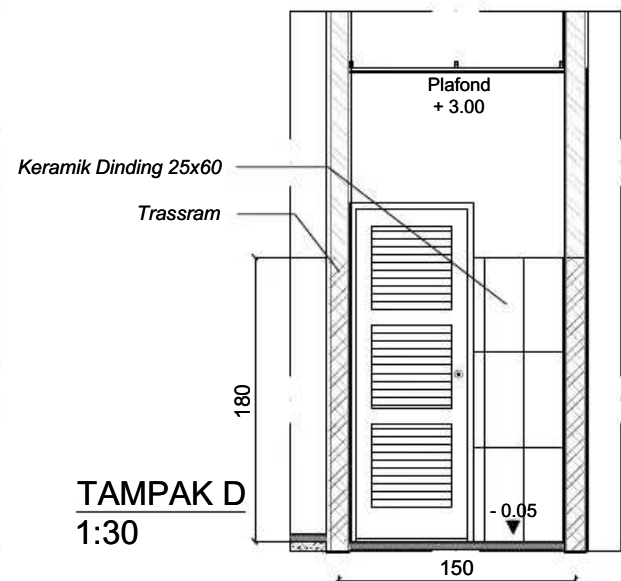


TAMPAK D
1:30


GAMBAR STRUKTUR

DENAH PONDASI
1:50


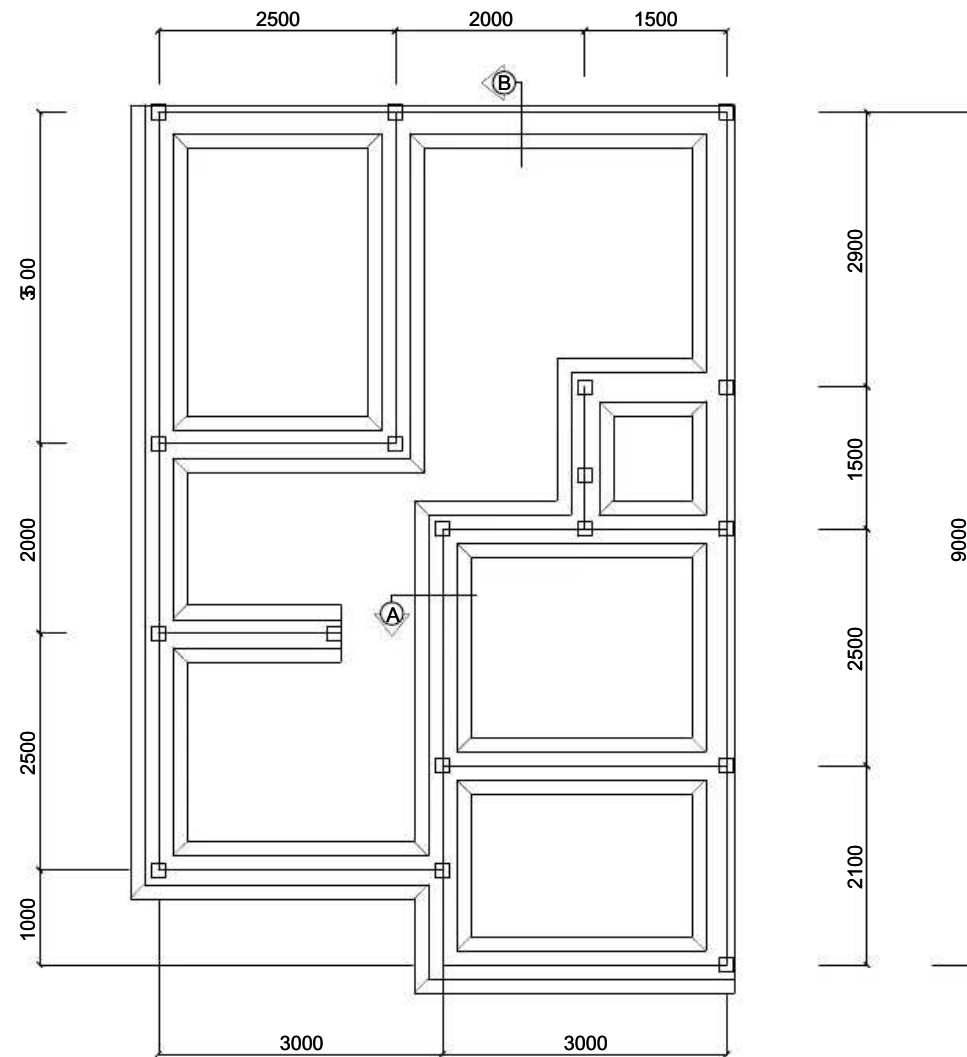


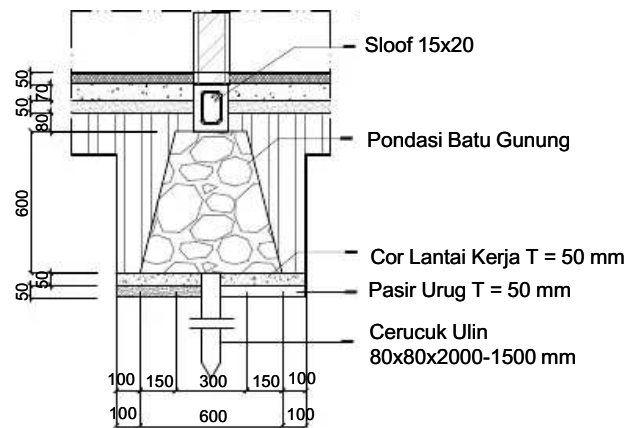

DETAIL A
1:20


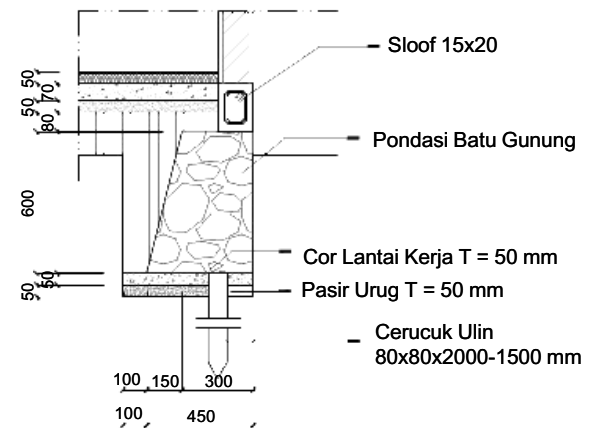


DETAIL B
1:20

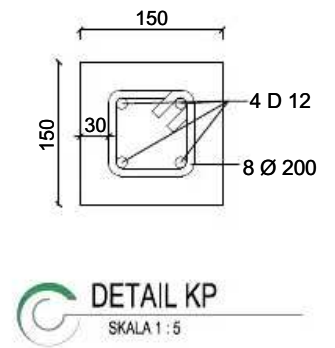
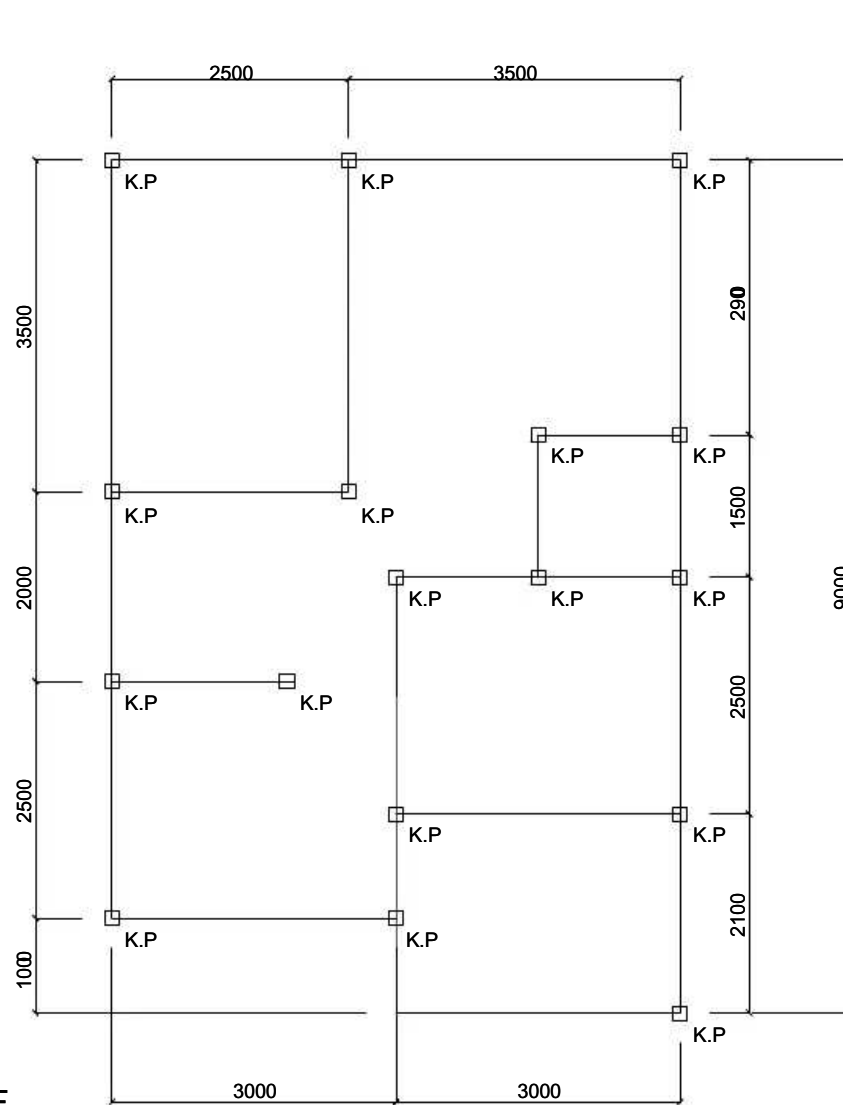


DENAH SLOOF
1:50



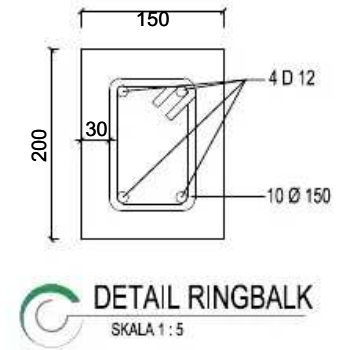
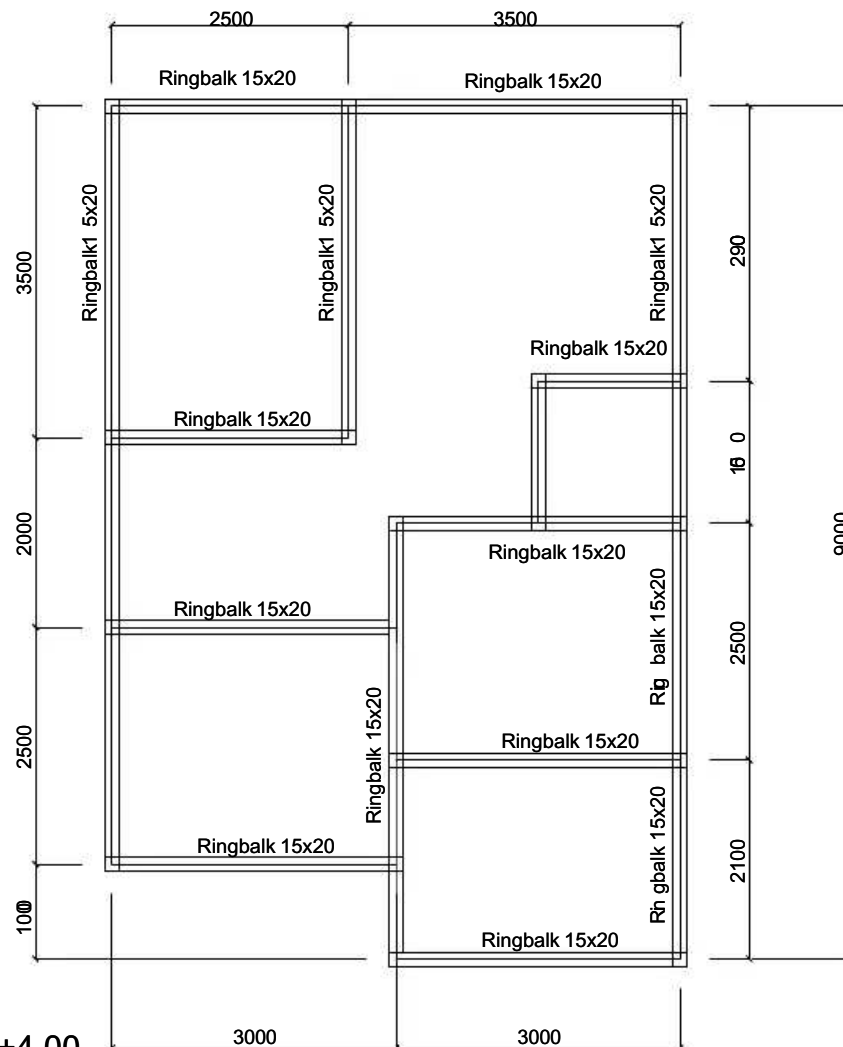


DENAH RINGBALK ELV +4.00
1:50

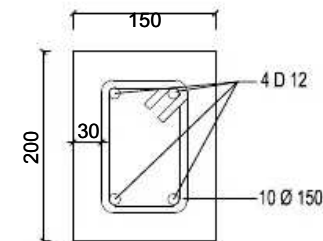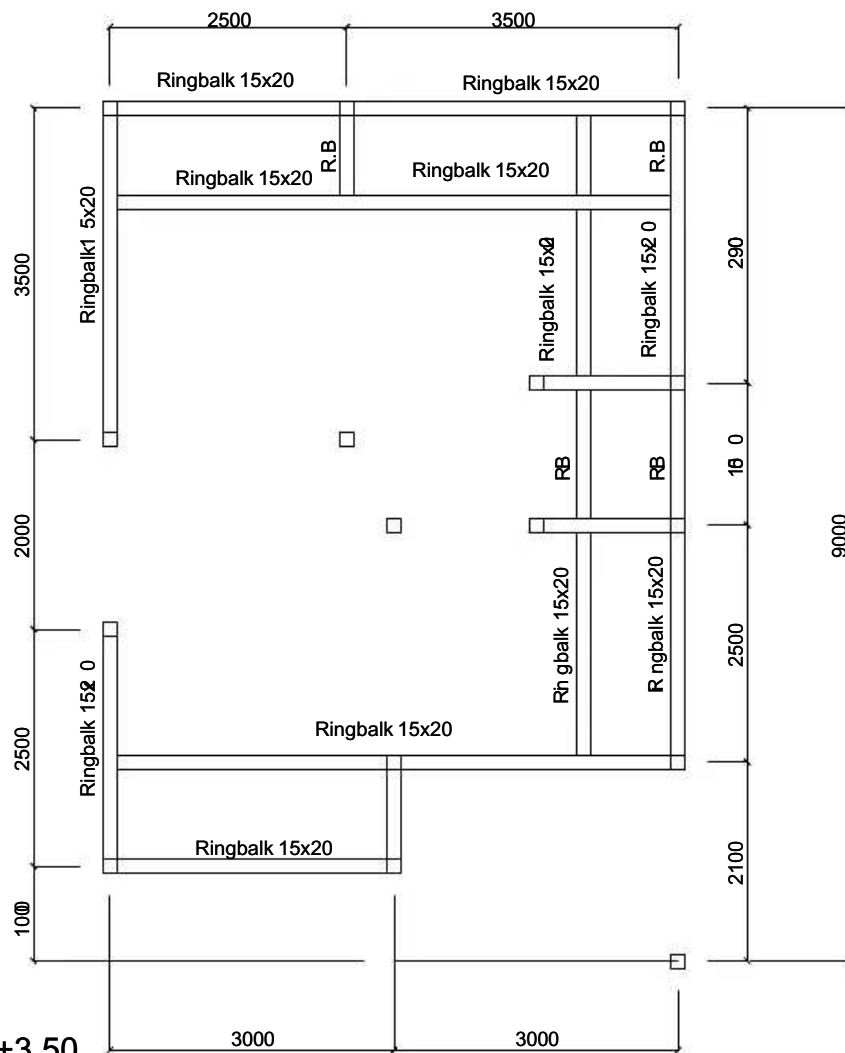


DETAIL RINGBALK
SKALA 1 : 5


DENAH RINGBALK ELV +3.50
1:50

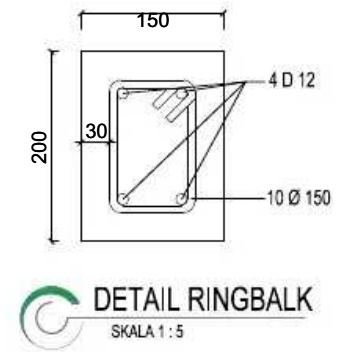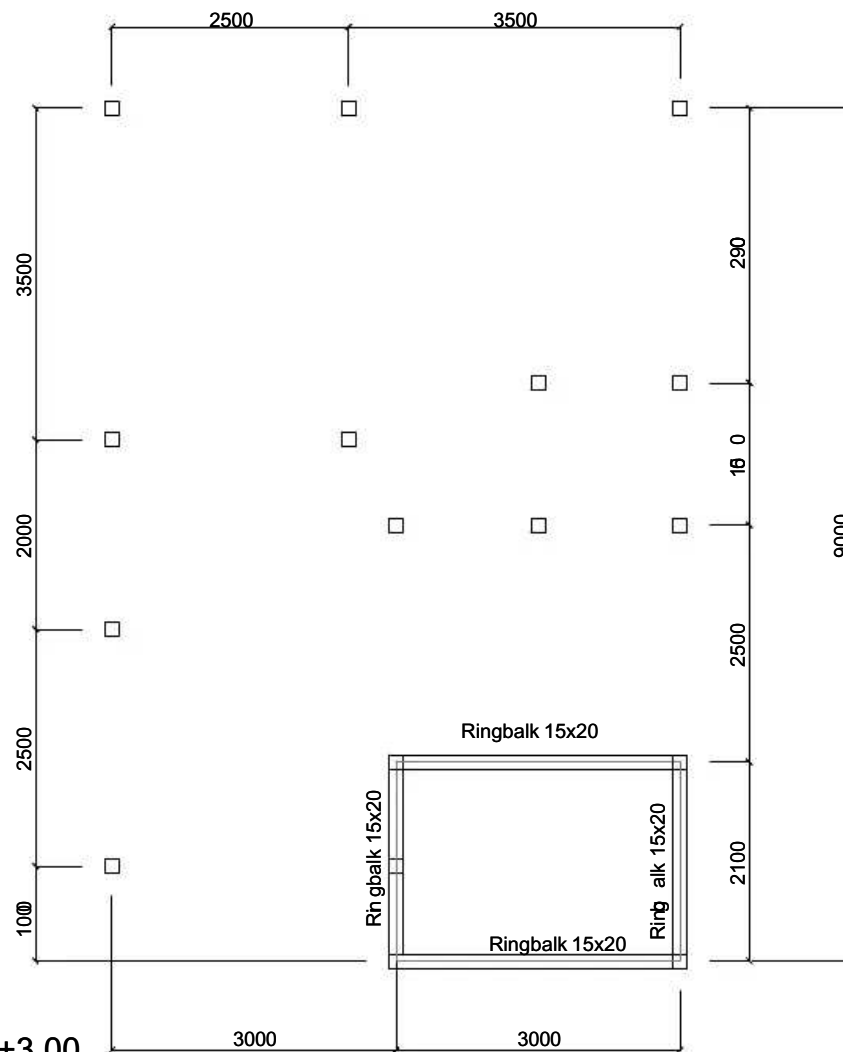

DENAH RINGBALK ELV +3.00
1:50

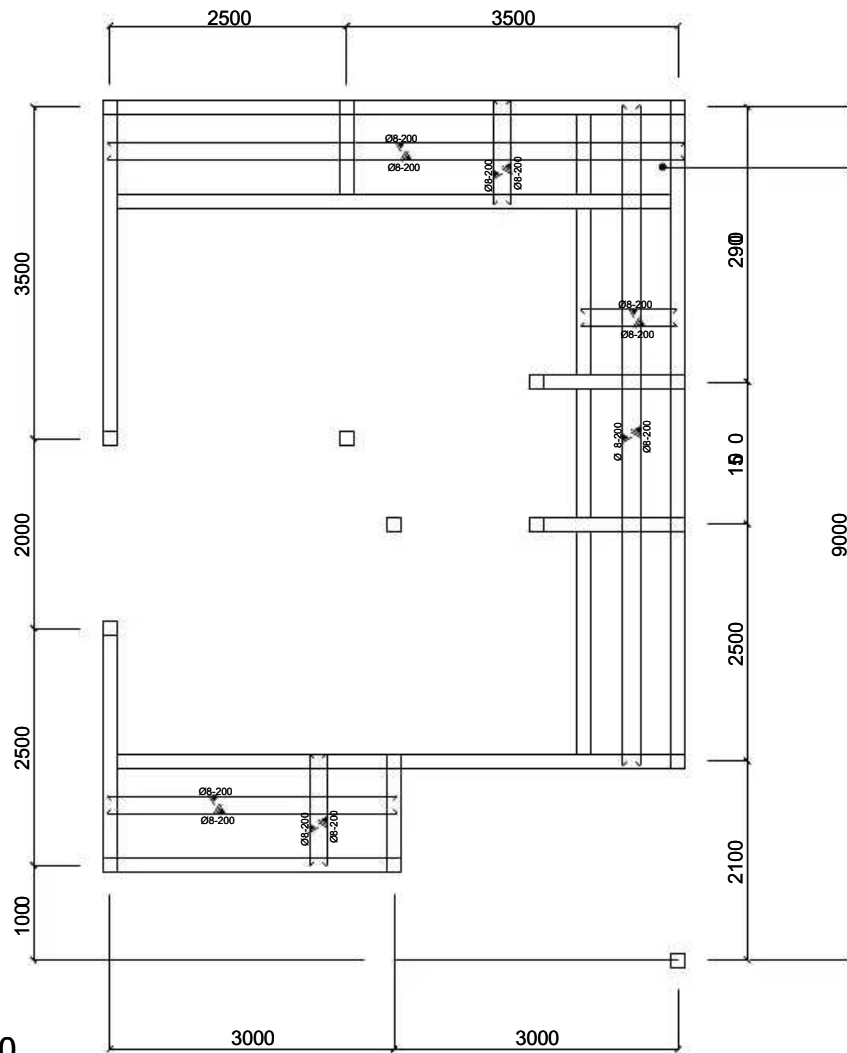


DENAH PELAT ELV +3.50
1:50

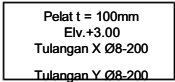

DENAH PELAT ELV +3.00
1:50


GAMBAR MEKANIKAL & ELEKTRIKAL

NO.	KETERANGAN	SYMBOL
1.	PIPA PVC 4"	— — — —
2.	PIPA PVC 2"	— · — · —
3.	PIPA PVC 1/2"	— · — · —
4.	FLOOR DRAIN	■

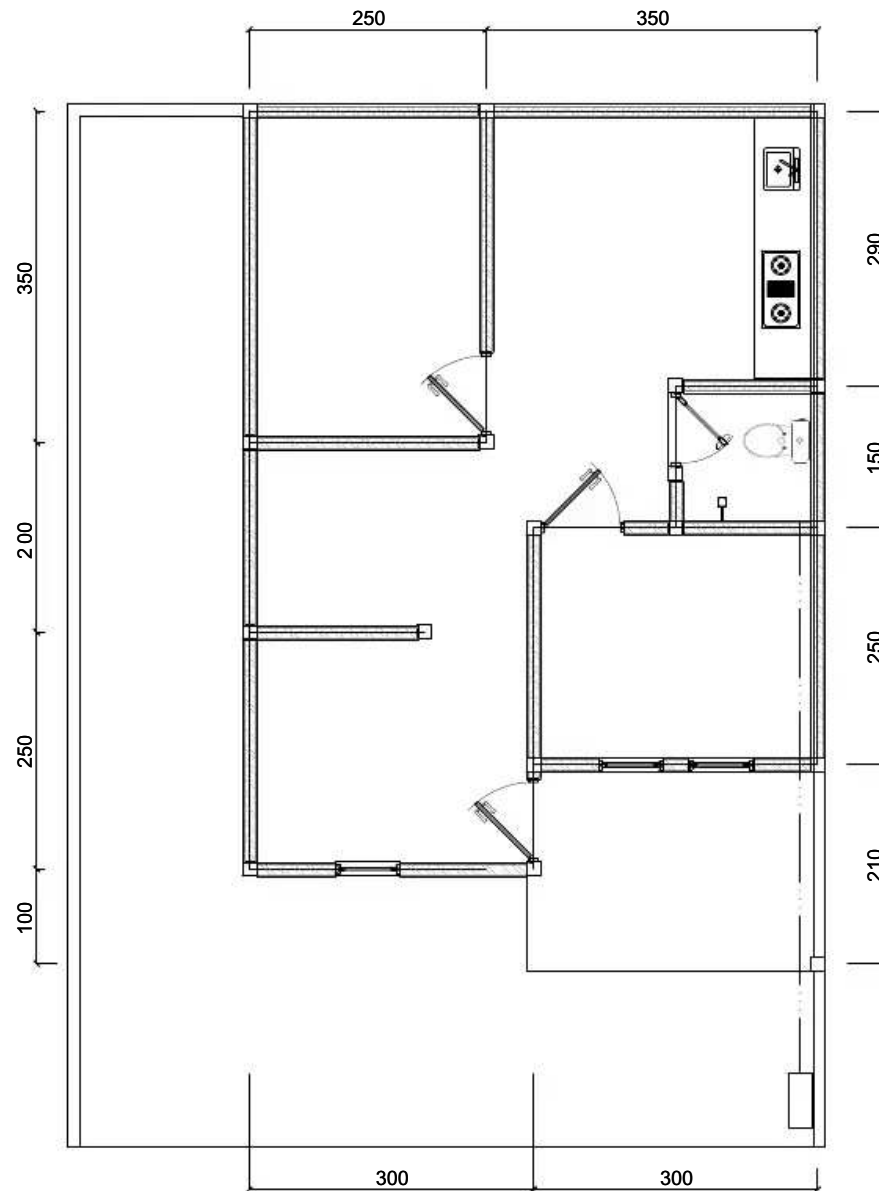


DENAH INSTALASI AIR BERSIH
1:50

NO.	KETERANGAN	SYMBOL
1.	PIPA PVC 4"	— — — —
2.	PIPA PVC 2"	— · — · —
3.	PIPA PVC 1/2"	— · · · —
4.	FLOOR DRAIN	■

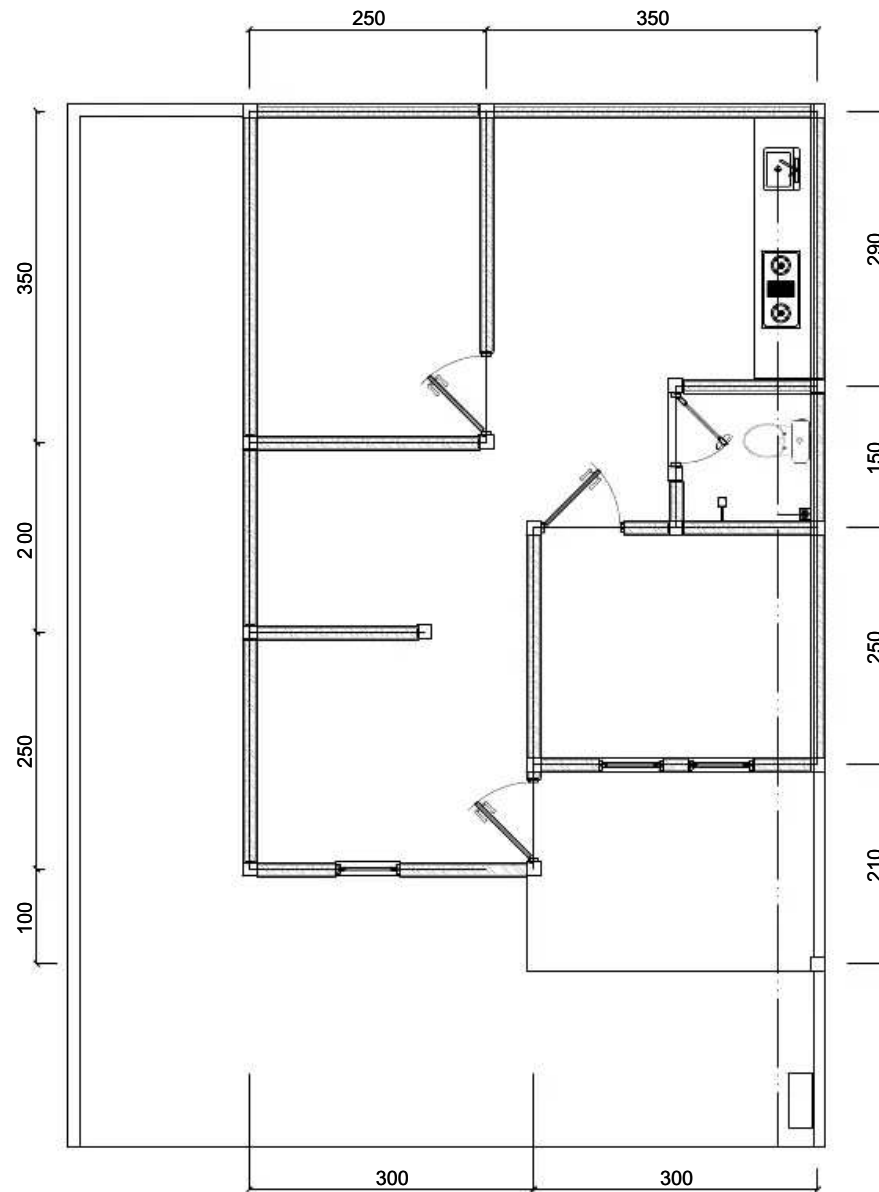


DENAH INSTALASI AIR KOTOR
1:50

NO.	KETERANGAN	SYMBOL
1.	PIPA PVC 4"	— — — — —
2.	PIPA PVC 2"	— · — · —
3.	PIPA PVC 1/2"	— · · · —
4.	FLOOR DRAIN	■

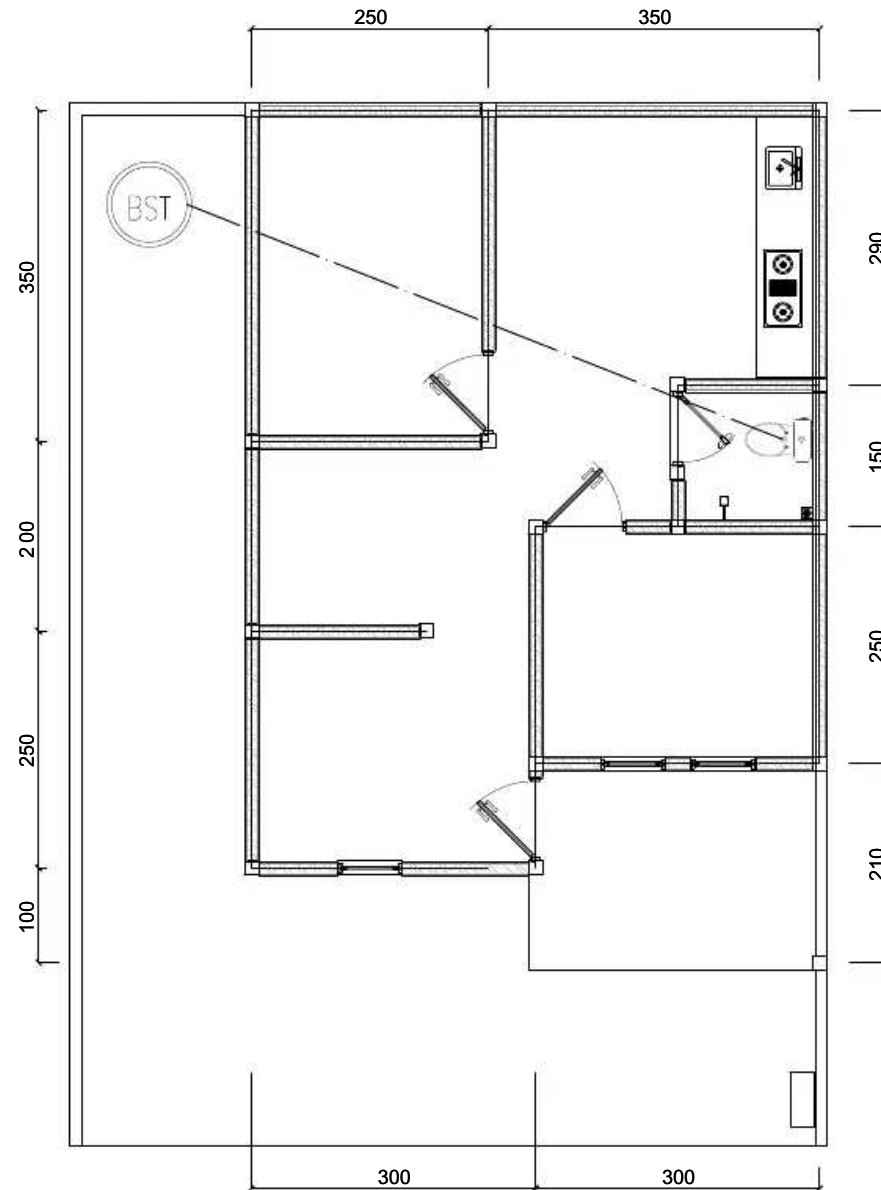


DENAH INSTALASI AIR KOTOR
1:50

KETERANGAN SIMBOL		JUMLAH
— —	KABEL LISTRIK	—
⬤	DOWN LIGHT	9 BH
⚡	SAKLAR TUNGGAL	3 BH
⚡	SAKLAR GANDA	3 BH
⚡	STOP KONTAK	6 BH
▬	PHB (MCB)	1 BH
⊠	METER LISTRIK	1 BH

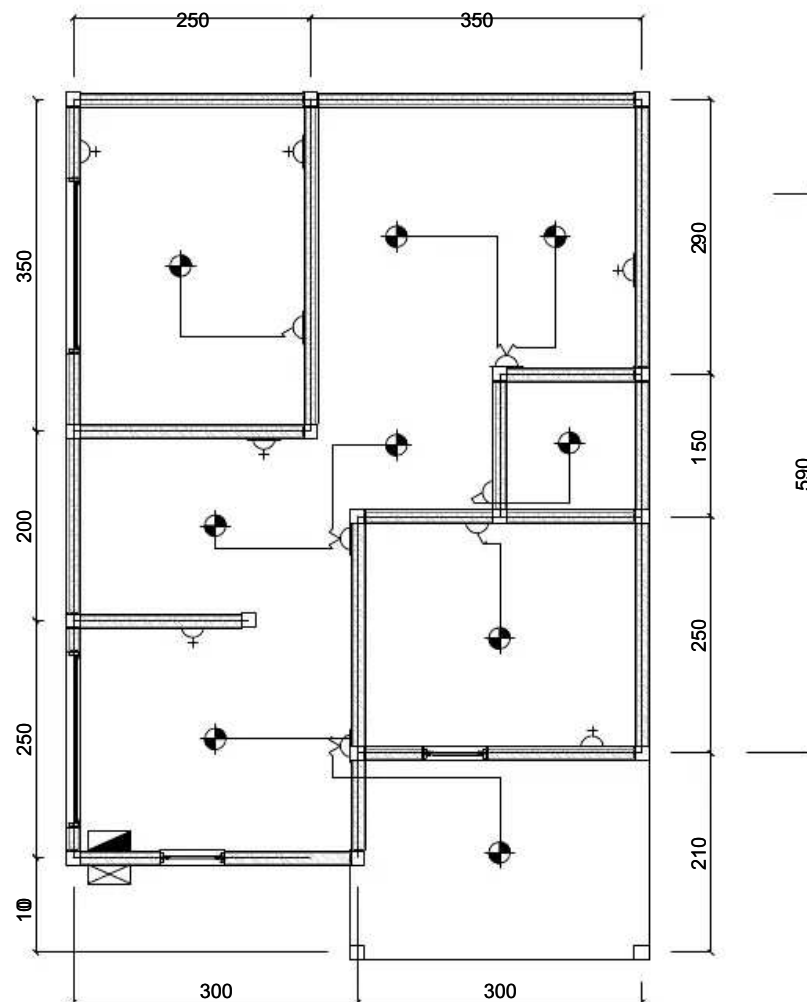

DENAH INSTALASI LISTRIK
1:50

KETERANGAN SIMBOL		JUMLAH
— —	KABEL LISTRIK	—
⬤	DOWN LIGHT	9 BH
⚡	SAKLAR TUNGGAL	3 BH
⚡	SAKLAR GANDA	3 BH
⚡	STOP KONTAK	6 BH
▬	PHB (MCB)	1 BH
⊠	METER LISTRIK	1 BH

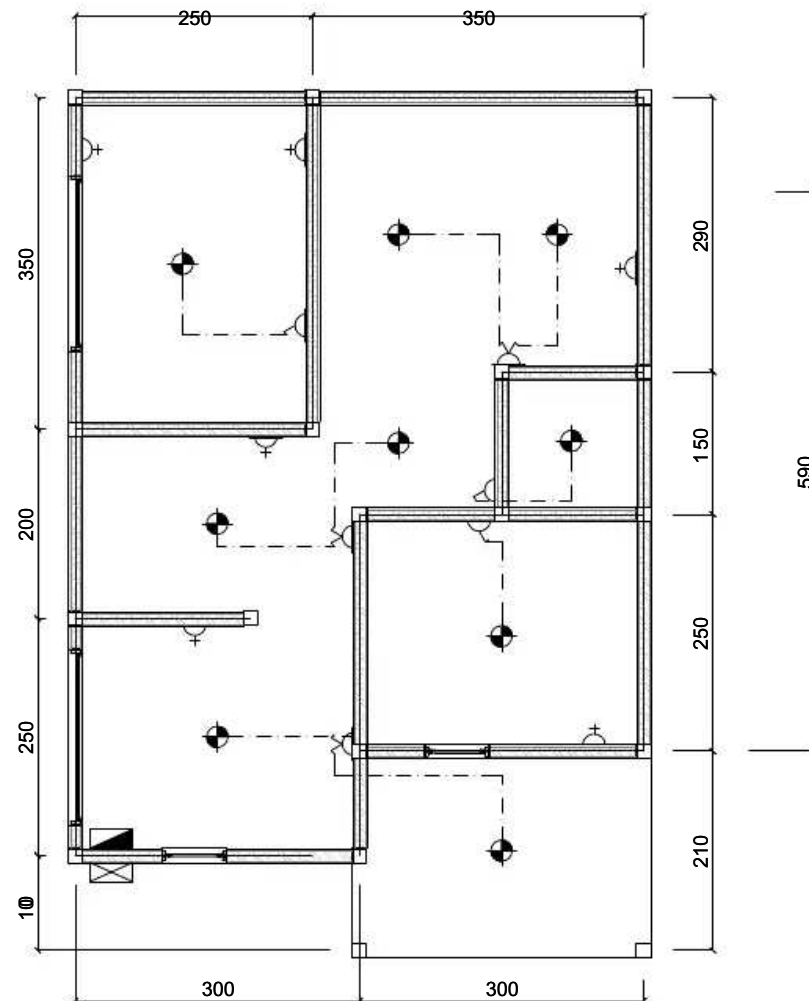

DENAH INSTALASI LISTRIK
1:50